


PARTS LIST

QTY	DESCRIPTION	PART NUMBER
1	93.5" 45° ENDS	SQ TUBE A500/A513 1.000 X 1.000 X 0.065
1	42" 45° END 35° END DRILL HOLE	SQ TUBE A500/A513 1.000 X 1.000 X 0.065
1	42" 45° END 35° END DRILL HOLE	SQ TUBE A500/A513 1.000 X 1.000 X 0.065

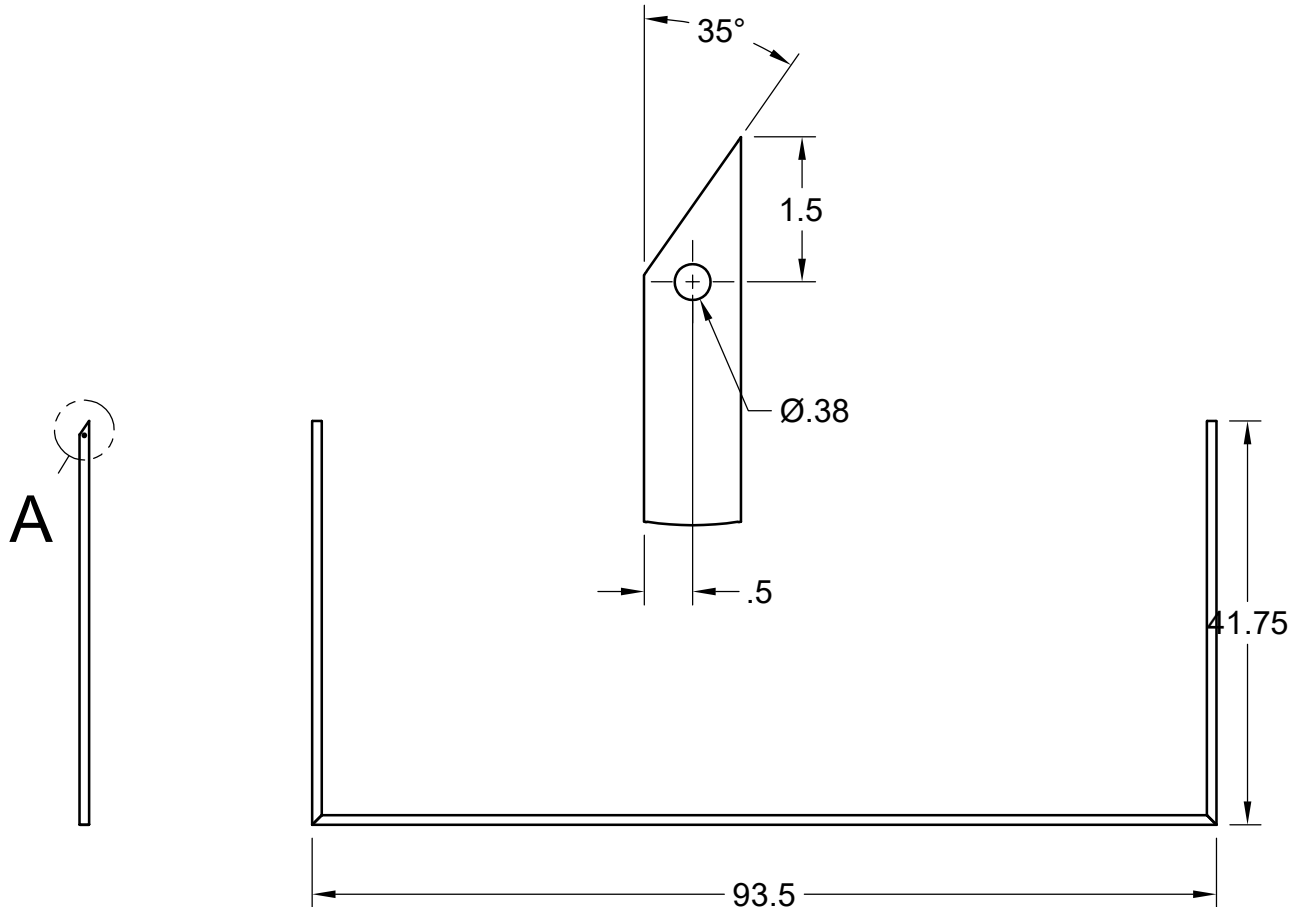

PROJECT

2024 Band Props

TITLE

Sideline Screen - Leg

APPROVED

CHECKED

SIZE

A

CODE

DWG NO

REV

DRAWN

Michael Hawkins 8/4/2024

SCALE 1:20

WEIGHT

SHEET 1/1